

ALZADO ROJO

ADOLFO RISOPATRÓN INZUNZA

PORTAFOLIO DE ARQUITECTURA • 2026



ARQUITECTURA & INVESTIGACIÓN

ADOLFO RISOPATRÓN INZUNZA

ARQUITECTO & M.SC. ARQUITECTURA SUSTENTABLE Y ENERGÍA

Arquitecto especializado en diseño paramétrico, prefabricación en madera y sustentabilidad. Enfoque integral que articula la optimización pasiva basada en datos con el rigor constructivo y la precisión del detalle ejecutivo para materializar arquitecturas de alto rendimiento ambiental y espacial.

SELECCIÓN DE PROYECTOS
ÍNDICE DE OBRAS

01	SISTEMA MODULAR EN MADERA MULTIFAMILY	2026
02	CENTRO CULTURAL & GALERÍA DE ARTE CONTEMPORÁNEO	2026
03	PARQUE CEMENTERIO EN PICHILEMU	2026
04	PLANIMETRÍA TÉCNICA & ESTÁNDAR EJECUTIVO	2024

01 SISTEMA MODULAR EN MADERA MULTIFAMILY 2026




Sistema constructivo prefabricado en madera contralaminada (CLT) y entramado ligero para vivienda colectiva en altura. Morfología bioclimática optimizada mediante modelado paramétrico para máxima captación solar pasiva, ventilación cruzada y drástica reducción de huella de carbono.



01 SISTEMA MODULAR EN MADERA MULTIFAMILY

2026

Despiece axonométrico del módulo prefabricado en CLT, detalle de encuentros estructurales para montaje en seco y simulación paramétrica de radiación solar y confort pasivo.

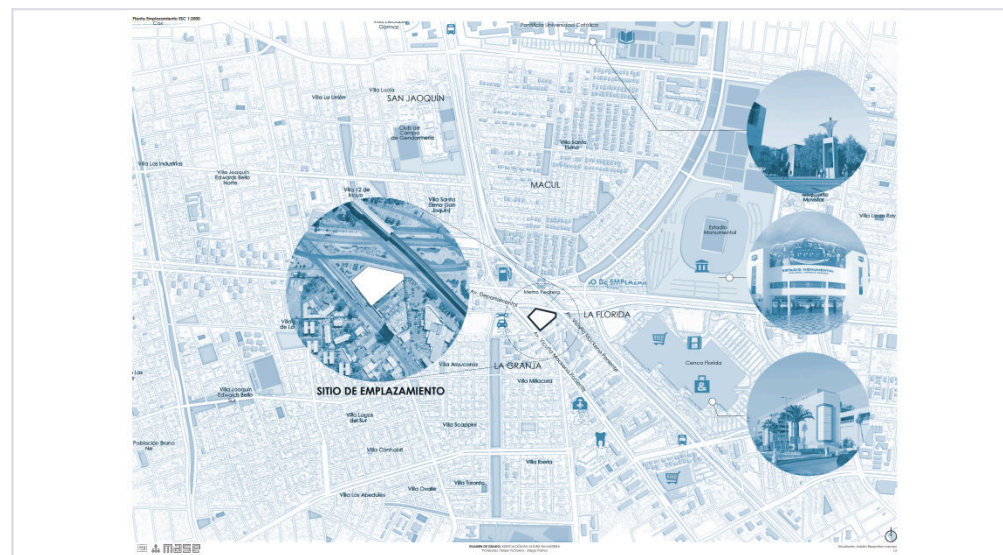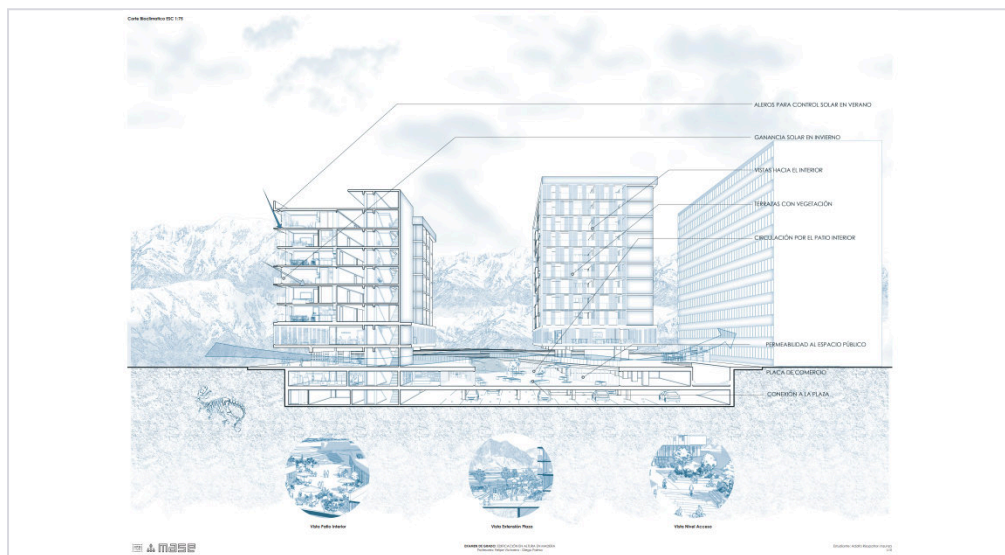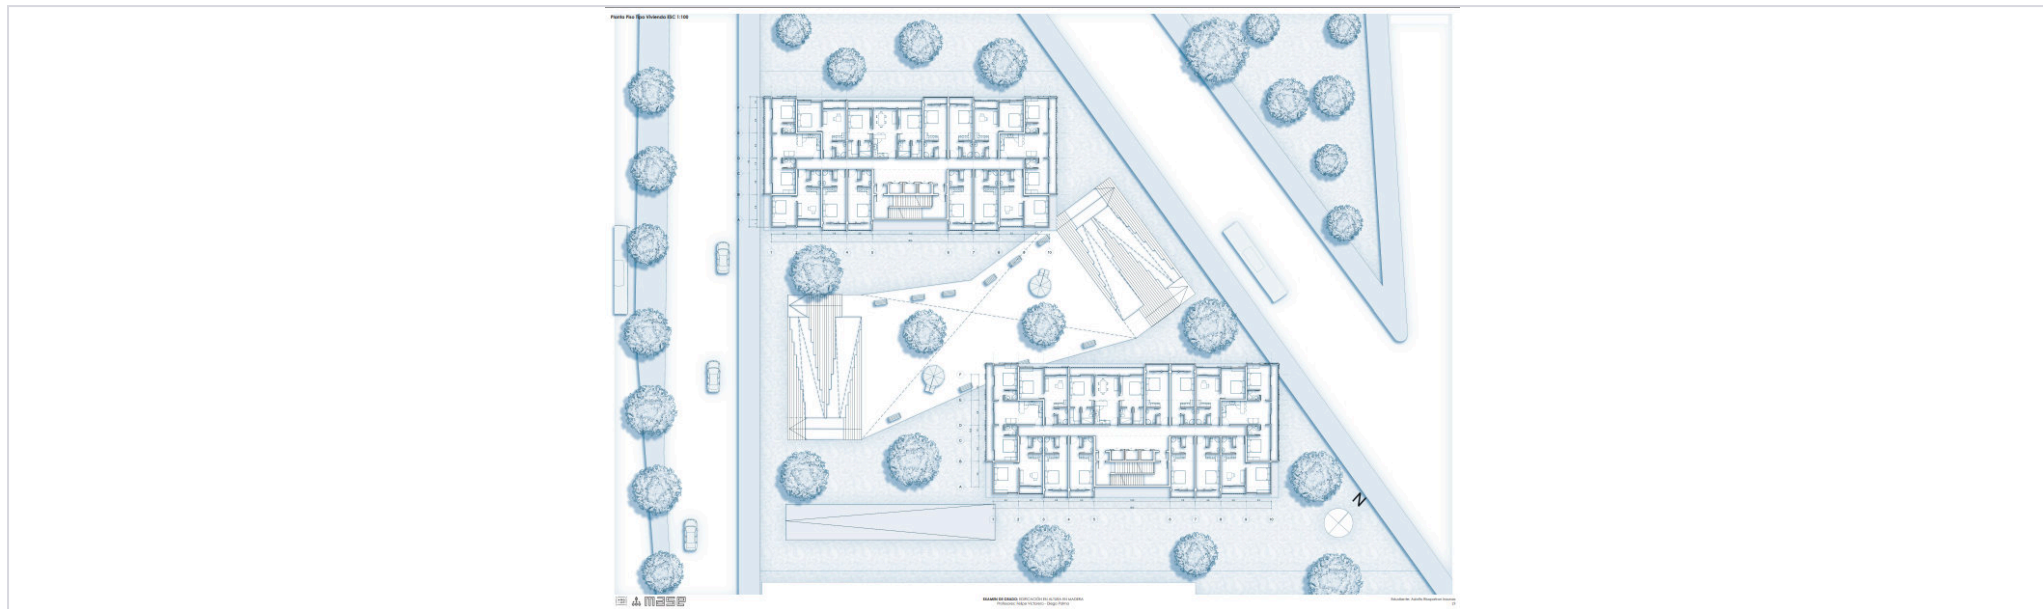

02 CENTRO CULTURAL & GALERÍA DE ARTE CONTEMPORÁNEO

2026




Intervención topográfica excavada que restituye el parque público en cubierta. Estructura monumental de vigas cajón en hormigón a la vista y lucarnas perimetrales que bañan las salas de exhibición con luz cenital difusa y homogénea, estabilizando pasivamente la temperatura interior de las galerías.



02 CENTRO CULTURAL & GALERÍA DE ARTE CONTEMPORÁNEO

2026

Planta general de arquitectura y secciones constructivas analíticas. Inserción topográfica bajo rasante y modulación de vigas y lucarnas cenitales para iluminación natural homogénea.

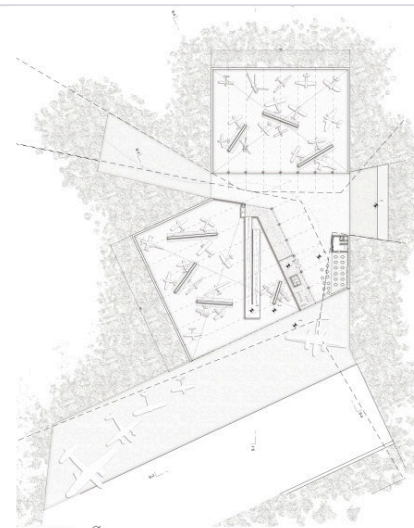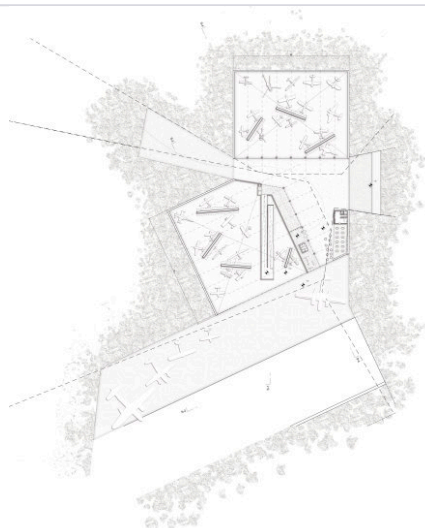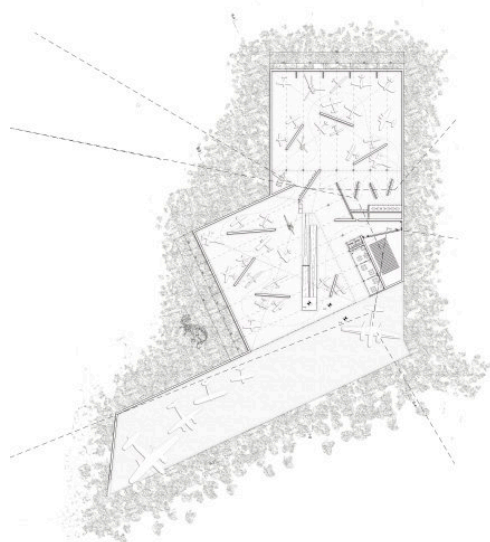

03 PARQUE CEMENTERIO EN PICHILEMU

2026

Propuesta paisajística y conmemorativa en la topografía costera de Pichilemu. Articulación de terrazas verdes, columbarios modulares de hormigón visto y muros de piedra integrados a la pendiente natural.



03 PARQUE CEMENTERIO EN PICHILEMU

2026


Perspectivas paisajísticas del conjunto memorial, articulación de terrazas verdes escalonadas y columbarios modulares de hormigón integrados a la ladera costera.



04 PLANIMETRÍA TÉCNICA & ESTÁNDAR EJECUTIVO

2024



Documentación ejecutiva de arquitectura y detalles constructivos a escala 1:50, 1:20 y 1:5. Rigurosa disciplina de valorización gráfica, coordinación de especialidades e identificación precisa de encuentros para faena y montaje en seco.

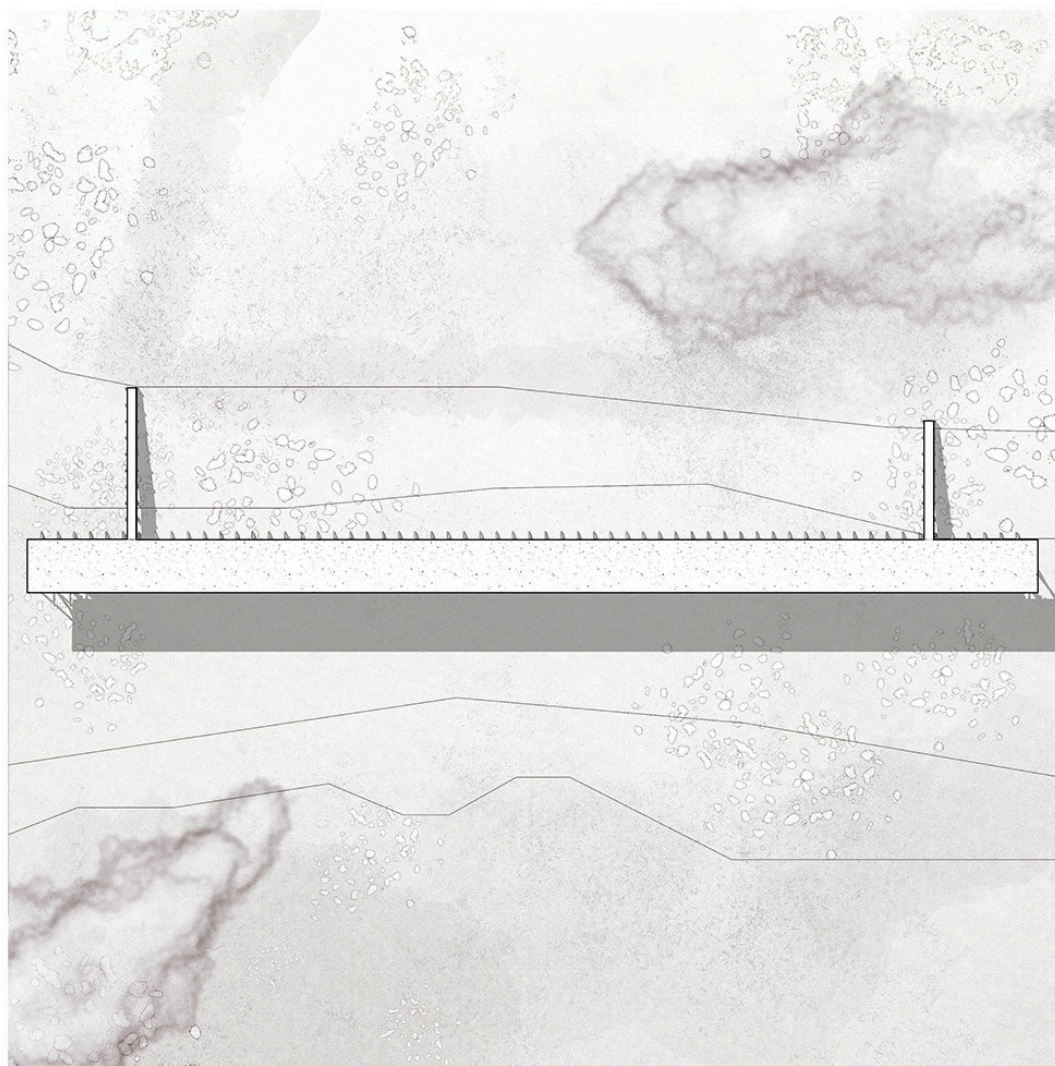

04 PLANIMETRÍA TÉCNICA & ESTÁNDAR EJECUTIVO

2024

Sección constructiva general por fachada a escala 1:20, detalles de encuentro milimétrico 1:5 y secuencia axonométrica de capas de aislamiento para montaje en seco.

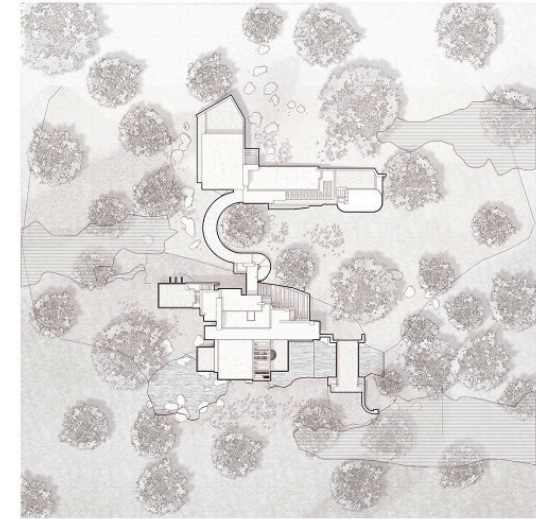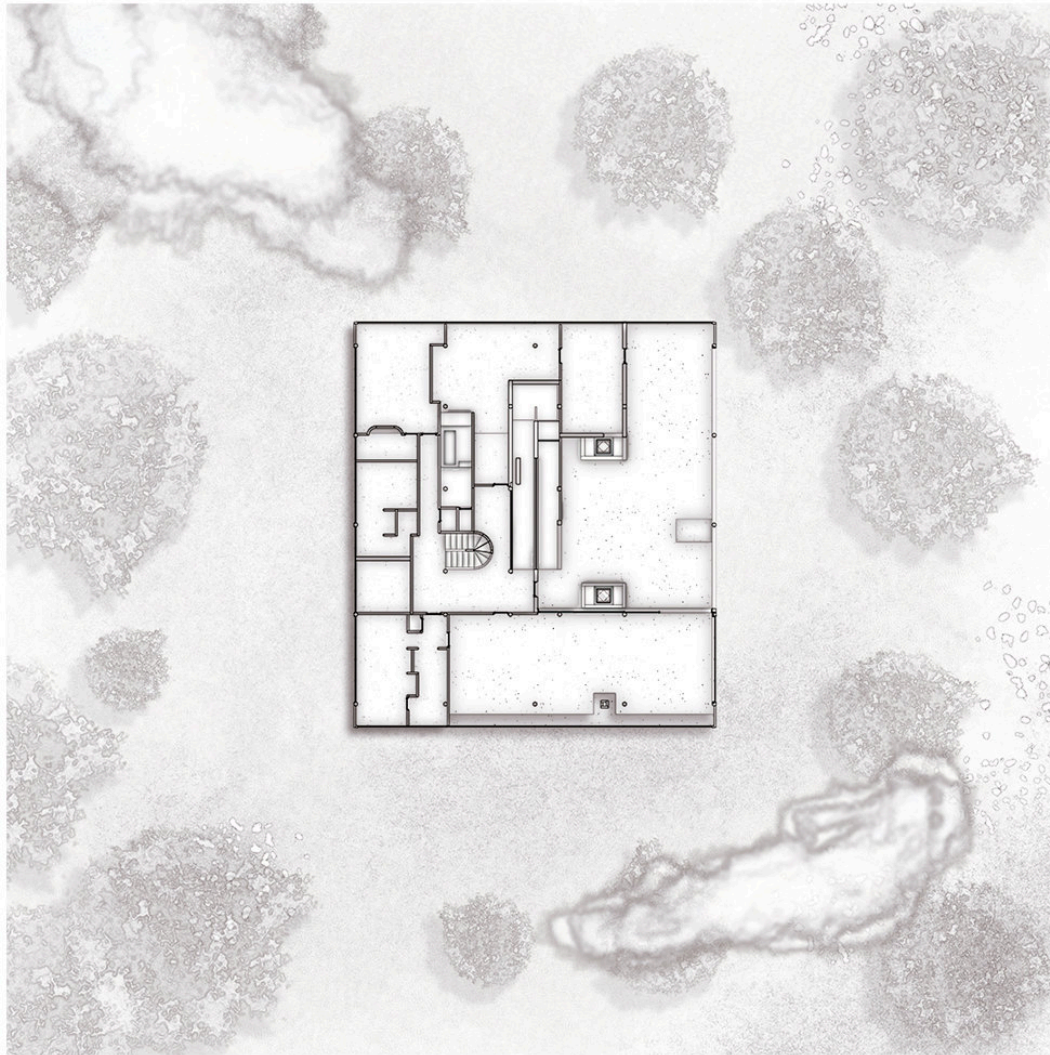



ALZADO ROJO



ADOLFO RISOPATRÓN INZUNZA

ARQUITECTO & M.SC. ARQUITECTURA SUSTENTABLE Y ENERGÍA

EMAIL	adolchilemods@gmail.com
LINKEDIN	linkedin.com/in/adolfo-risopatron-inzunza
PORTAFOLIO WEB	ar-arq.cl
TELÉFONO	+56 9 8419 6391
UBICACIÓN	Santiago de Chile

