ALZADO ROJO

ADOLFO RISOPATRÓN INZUNZA

PORTAFOLIO DE ARQUITECTURA · 2026



INVESTIGACIÓN APLICADA

ADOLFO RISOPATRÓN INZUNZA

ARQUITECTO Y M.SC. ARQUITECTURA SUSTENTABLE Y ENERGÍA

Arquitecto especializado en diseño paramétrico, prefabricación en madera y sustentabilidad. Enfoque integral que articula la optimización pasiva basada en datos con el rigor constructivo y la precisión del detalle ejecutivo para materializar arquitecturas de alto rendimiento ambiental y espacial.

SELECCIÓN DE PROYECTOS

ÍNDICE DE OBRAS

01	SISTEMA MODULAR EN MADERA MULTIFAMILY	2026
02	CENTRO CULTURAL CONTEMPORÁNEO	2026
03	PARQUE CEMENTERIO EN PICHILEMU	2026
04	PLANIMETRÍA TÉCNICA EJECUTIVA	2024

01 SISTEMA MODULAR EN MADERA MULTIFAMILY

2026


Sistema constructivo prefabricado en madera contralaminada (CLT) y entramado ligero para vivienda colectiva en altura. Morfología bioclimática optimizada mediante modelado paramétrico para máxima captación solar pasiva, ventilación cruzada y drástica reducción de huella de carbono.





01 SISTEMA MODULAR EN MADERA MULTIFAMILY

2026

Despiece axonométrico del módulo prefabricado en CLT, detalle de encuentros estructurales para montaje en seco y simulación paramétrica de radiación solar y confort pasivo.

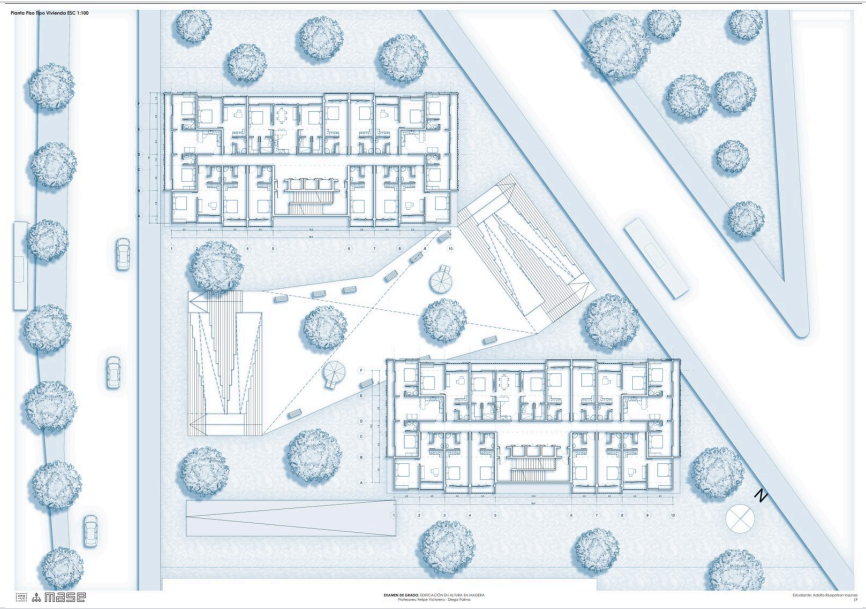

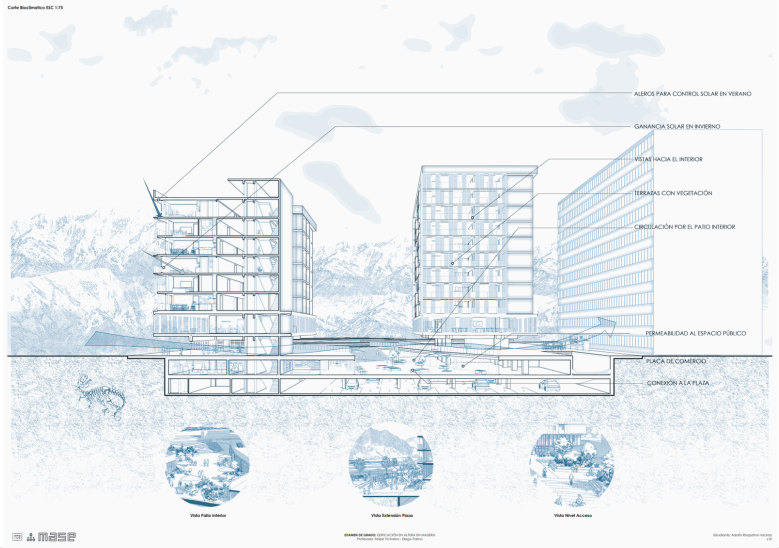


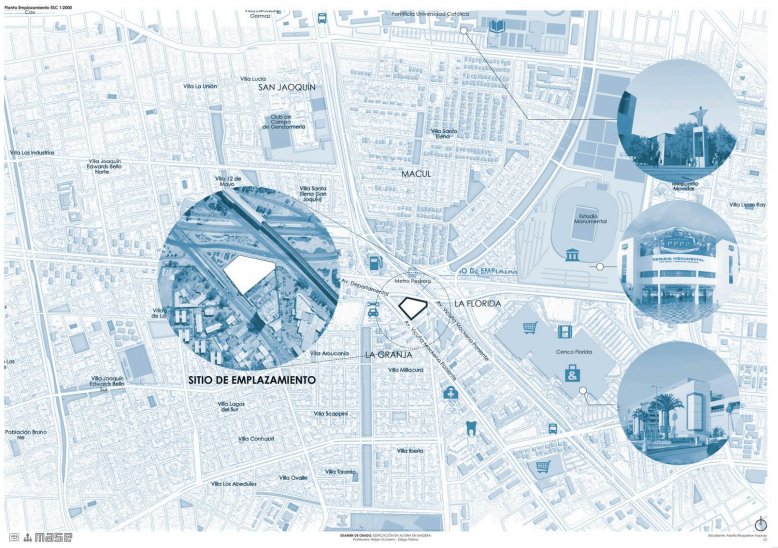

02 CENTRO CULTURAL CONTEMPORÁNEO

2026

Intervención topográfica excavada que restituye el parque público en cubierta. Estructura monumental de vigas cajón en hormigón a la vista y lucarnas perimetrales que bañan las salas de exhibición con luz cenital difusa y homogénea, estabilizando pasivamente la temperatura interior de las galerías.

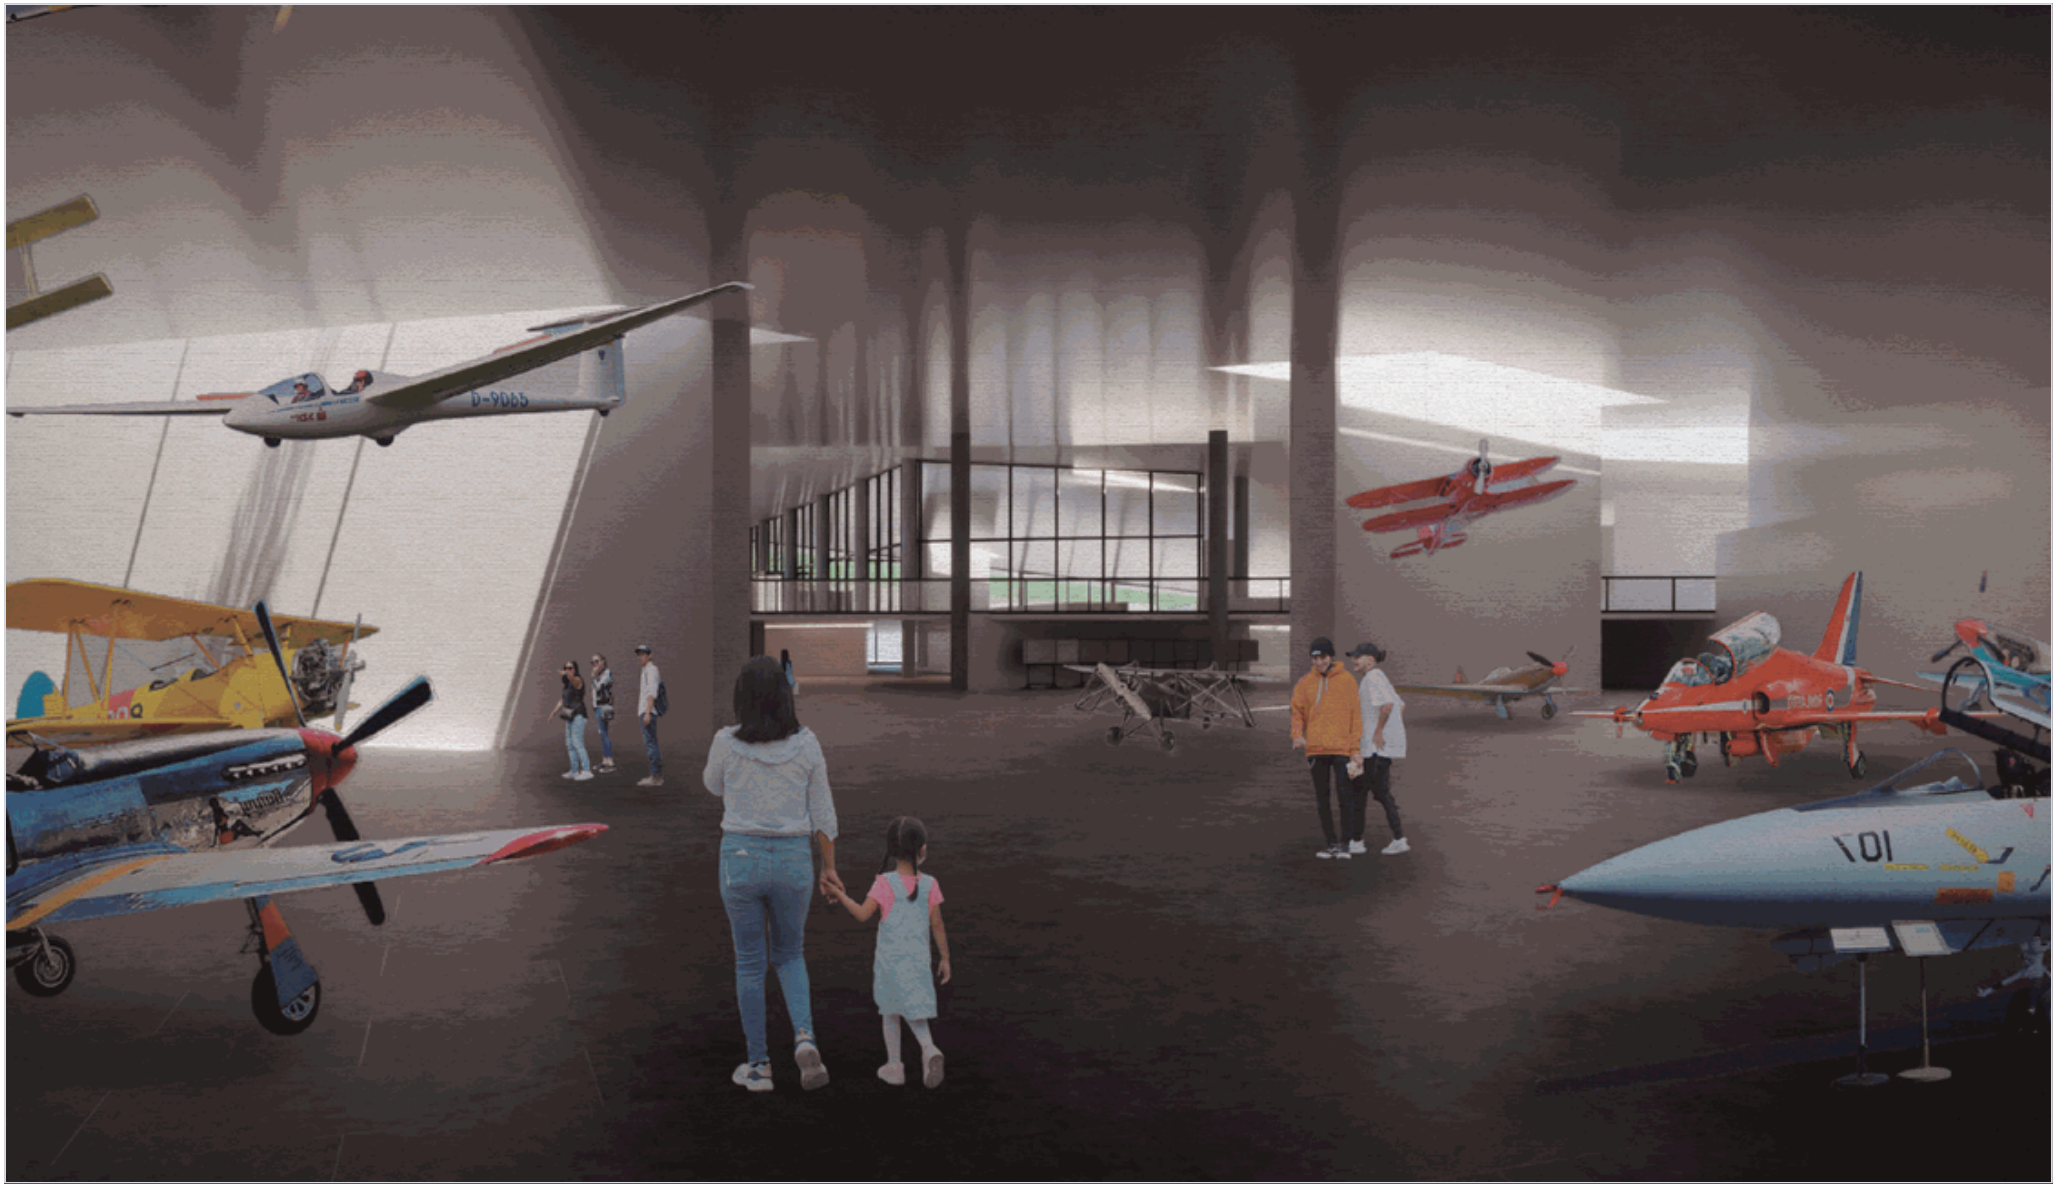



CENTRO CULTURAL — VISTA DE LA NAVE EXPOSITIVA PRINCIPAL


02 CENTRO CULTURAL CONTEMPORÁNEO

2026

Planta general de arquitectura y secciones constructivas analíticas. Inserción topográfica bajo rasante y modulación de vigas y lucarnas cenitales para iluminación natural homogénea.

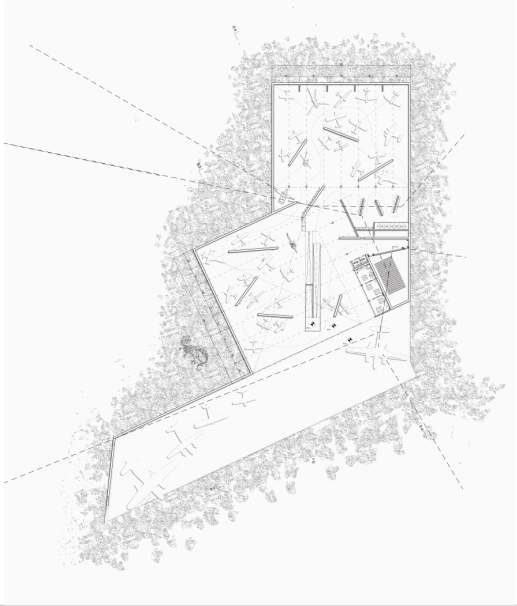

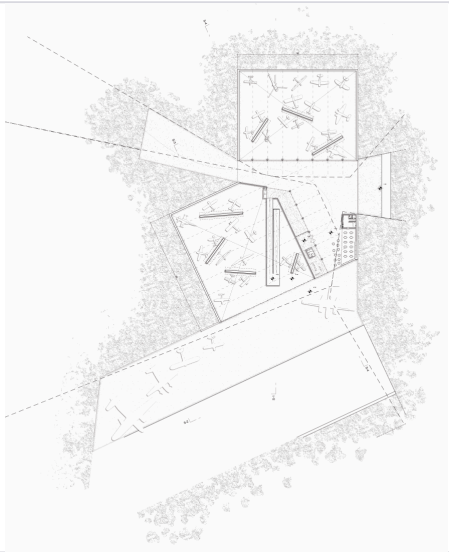

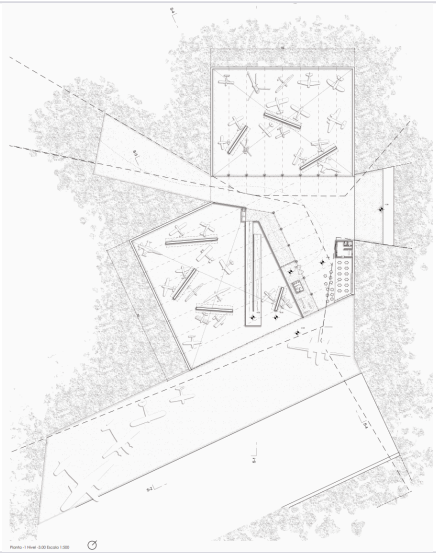

03 PARQUE CEMENTERIO EN PICHILEMU

2026

Propuesta paisajística y conmemorativa en la topografía costera de Pichilemu. Articulación de terrazas verdes, columbarios modulares de hormigón visto y muros de piedra integrados a la pendiente natural.



03 PARQUE CEMENTERIO EN PICHILEMU

2026

Perspectivas paisajísticas del conjunto memorial, articulación de terrazas verdes escalonadas y columbarios modulares de hormigón integrados a la ladera costera.








04 PLANIMETRÍA TÉCNICA EJECUTIVA

2024


Documentación ejecutiva de arquitectura y detalles constructivos a escala 1:50, 1:20 y 1:5. Rigurosa disciplina de valorización gráfica, coordinación de especialidades e identificación precisa de encuentros para faena y montaje en seco.

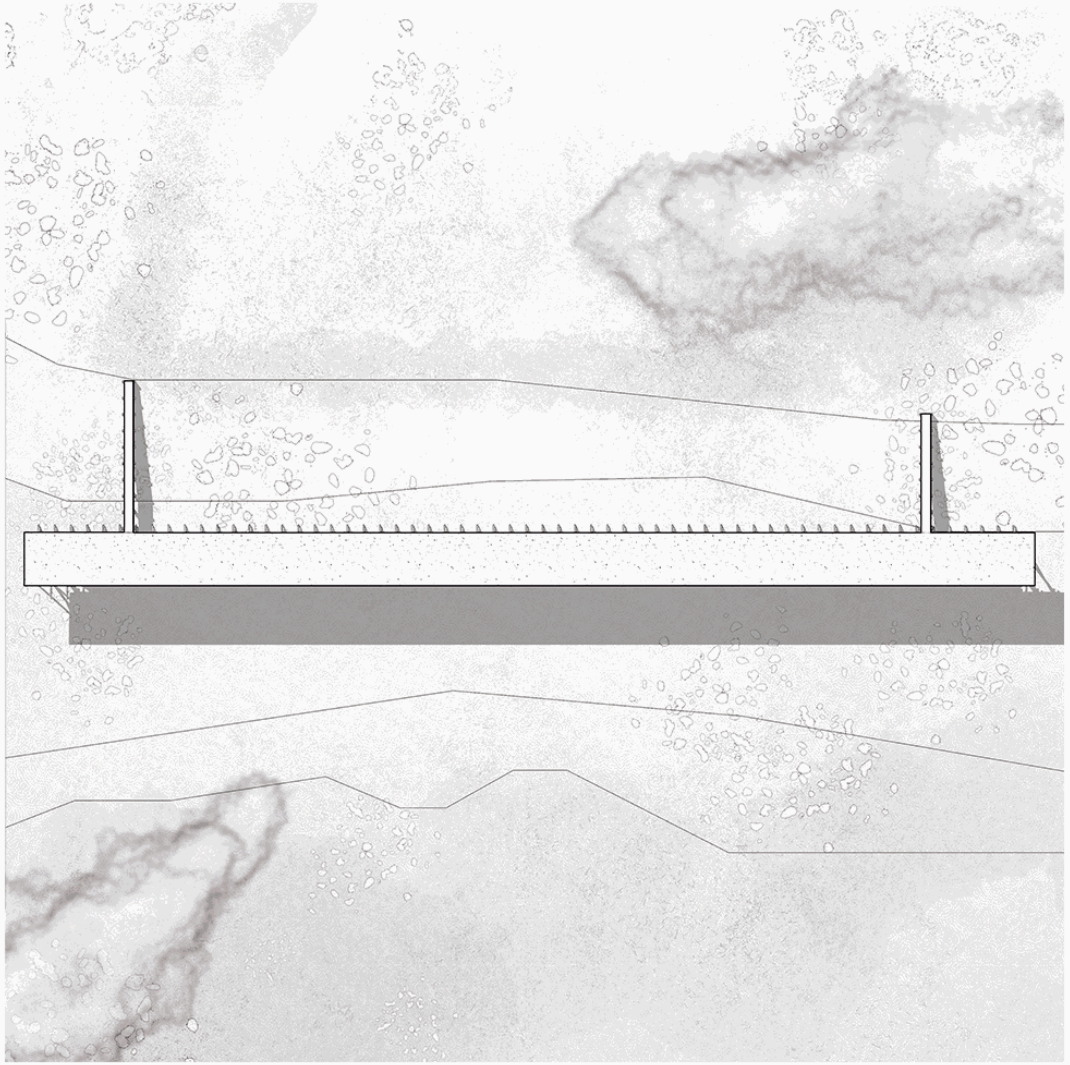


04 PLANIMETRÍA TÉCNICA EJECUTIVA

2024

Sección constructiva general por fachada a escala 1:20, detalles de encuentro milimétrico 1:5 y secuencia axonométrica de capas de aislamiento para montaje en seco.

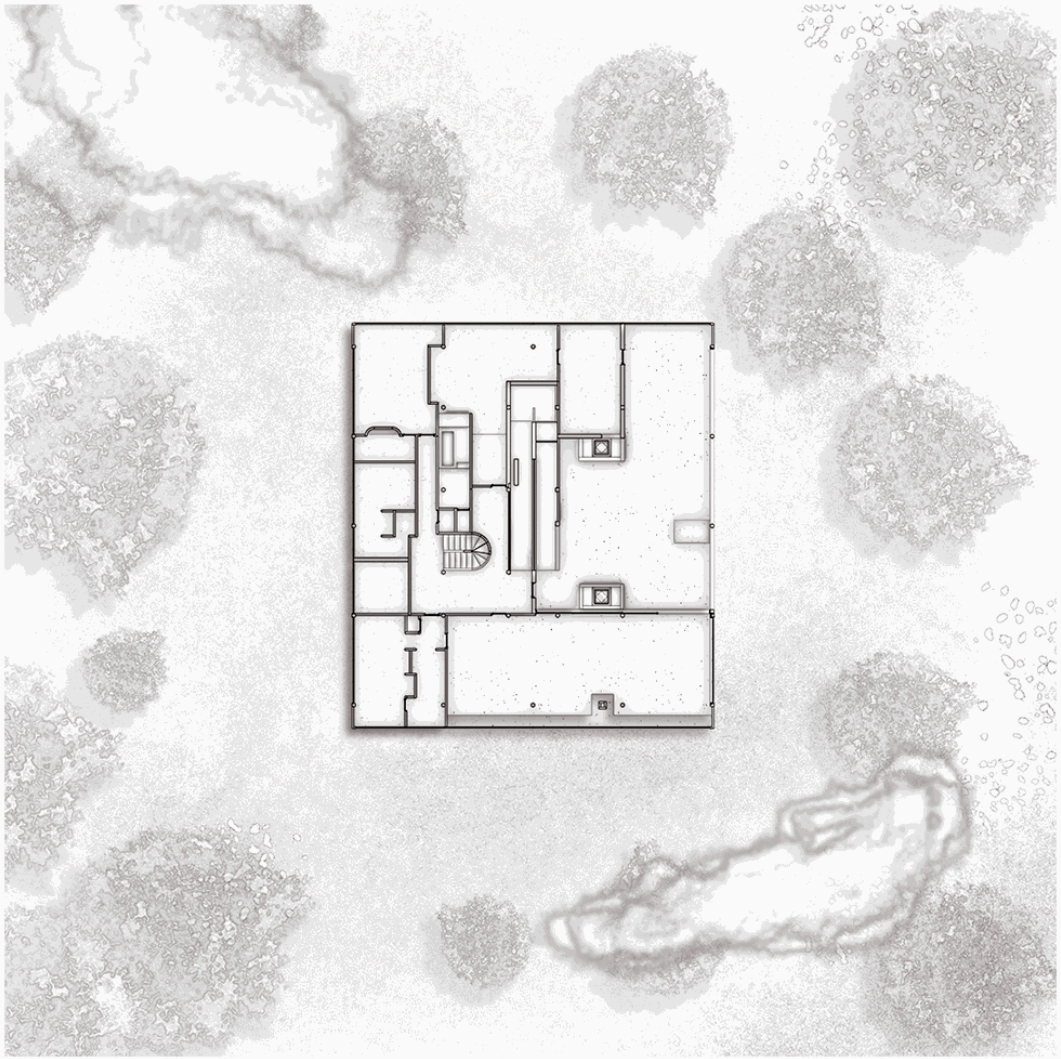

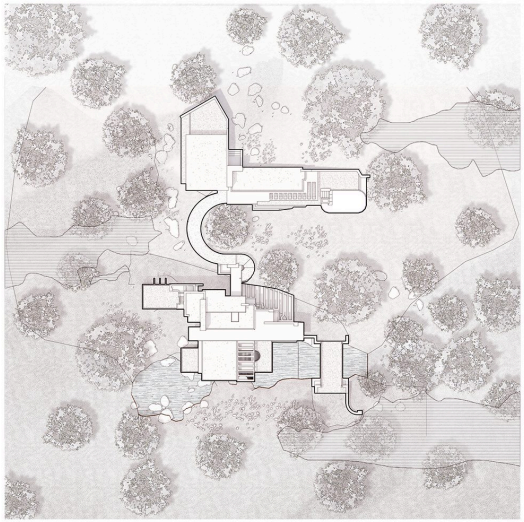



ALZADO ROJO

ADOLFO RISOPATRÓN INZUNZA

ARQUITECTO Y M.SC. ARQUITECTURA SUSTENTABLE Y ENERGÍA

EMAIL	adolchilemods@gmail.com
LINKEDIN	linkedin.com/in/adolfo-risopatron-inzunza
PORTAFOLIO WEB	ar-arq.cl
TELÉFONO	+56 9 6203 2766
UBICACIÓN	Santiago de Chile

En ALZADO ROJO utilizamos cookies técnicas estrictamente necesarias para la navegación y personalización de preferencias. Puede aceptar todas las funciones o limitar su uso a las necesarias. Consulte los detalles en nuestra Política de Cookies.
SOLO NECESARIAS ACEPTAR